


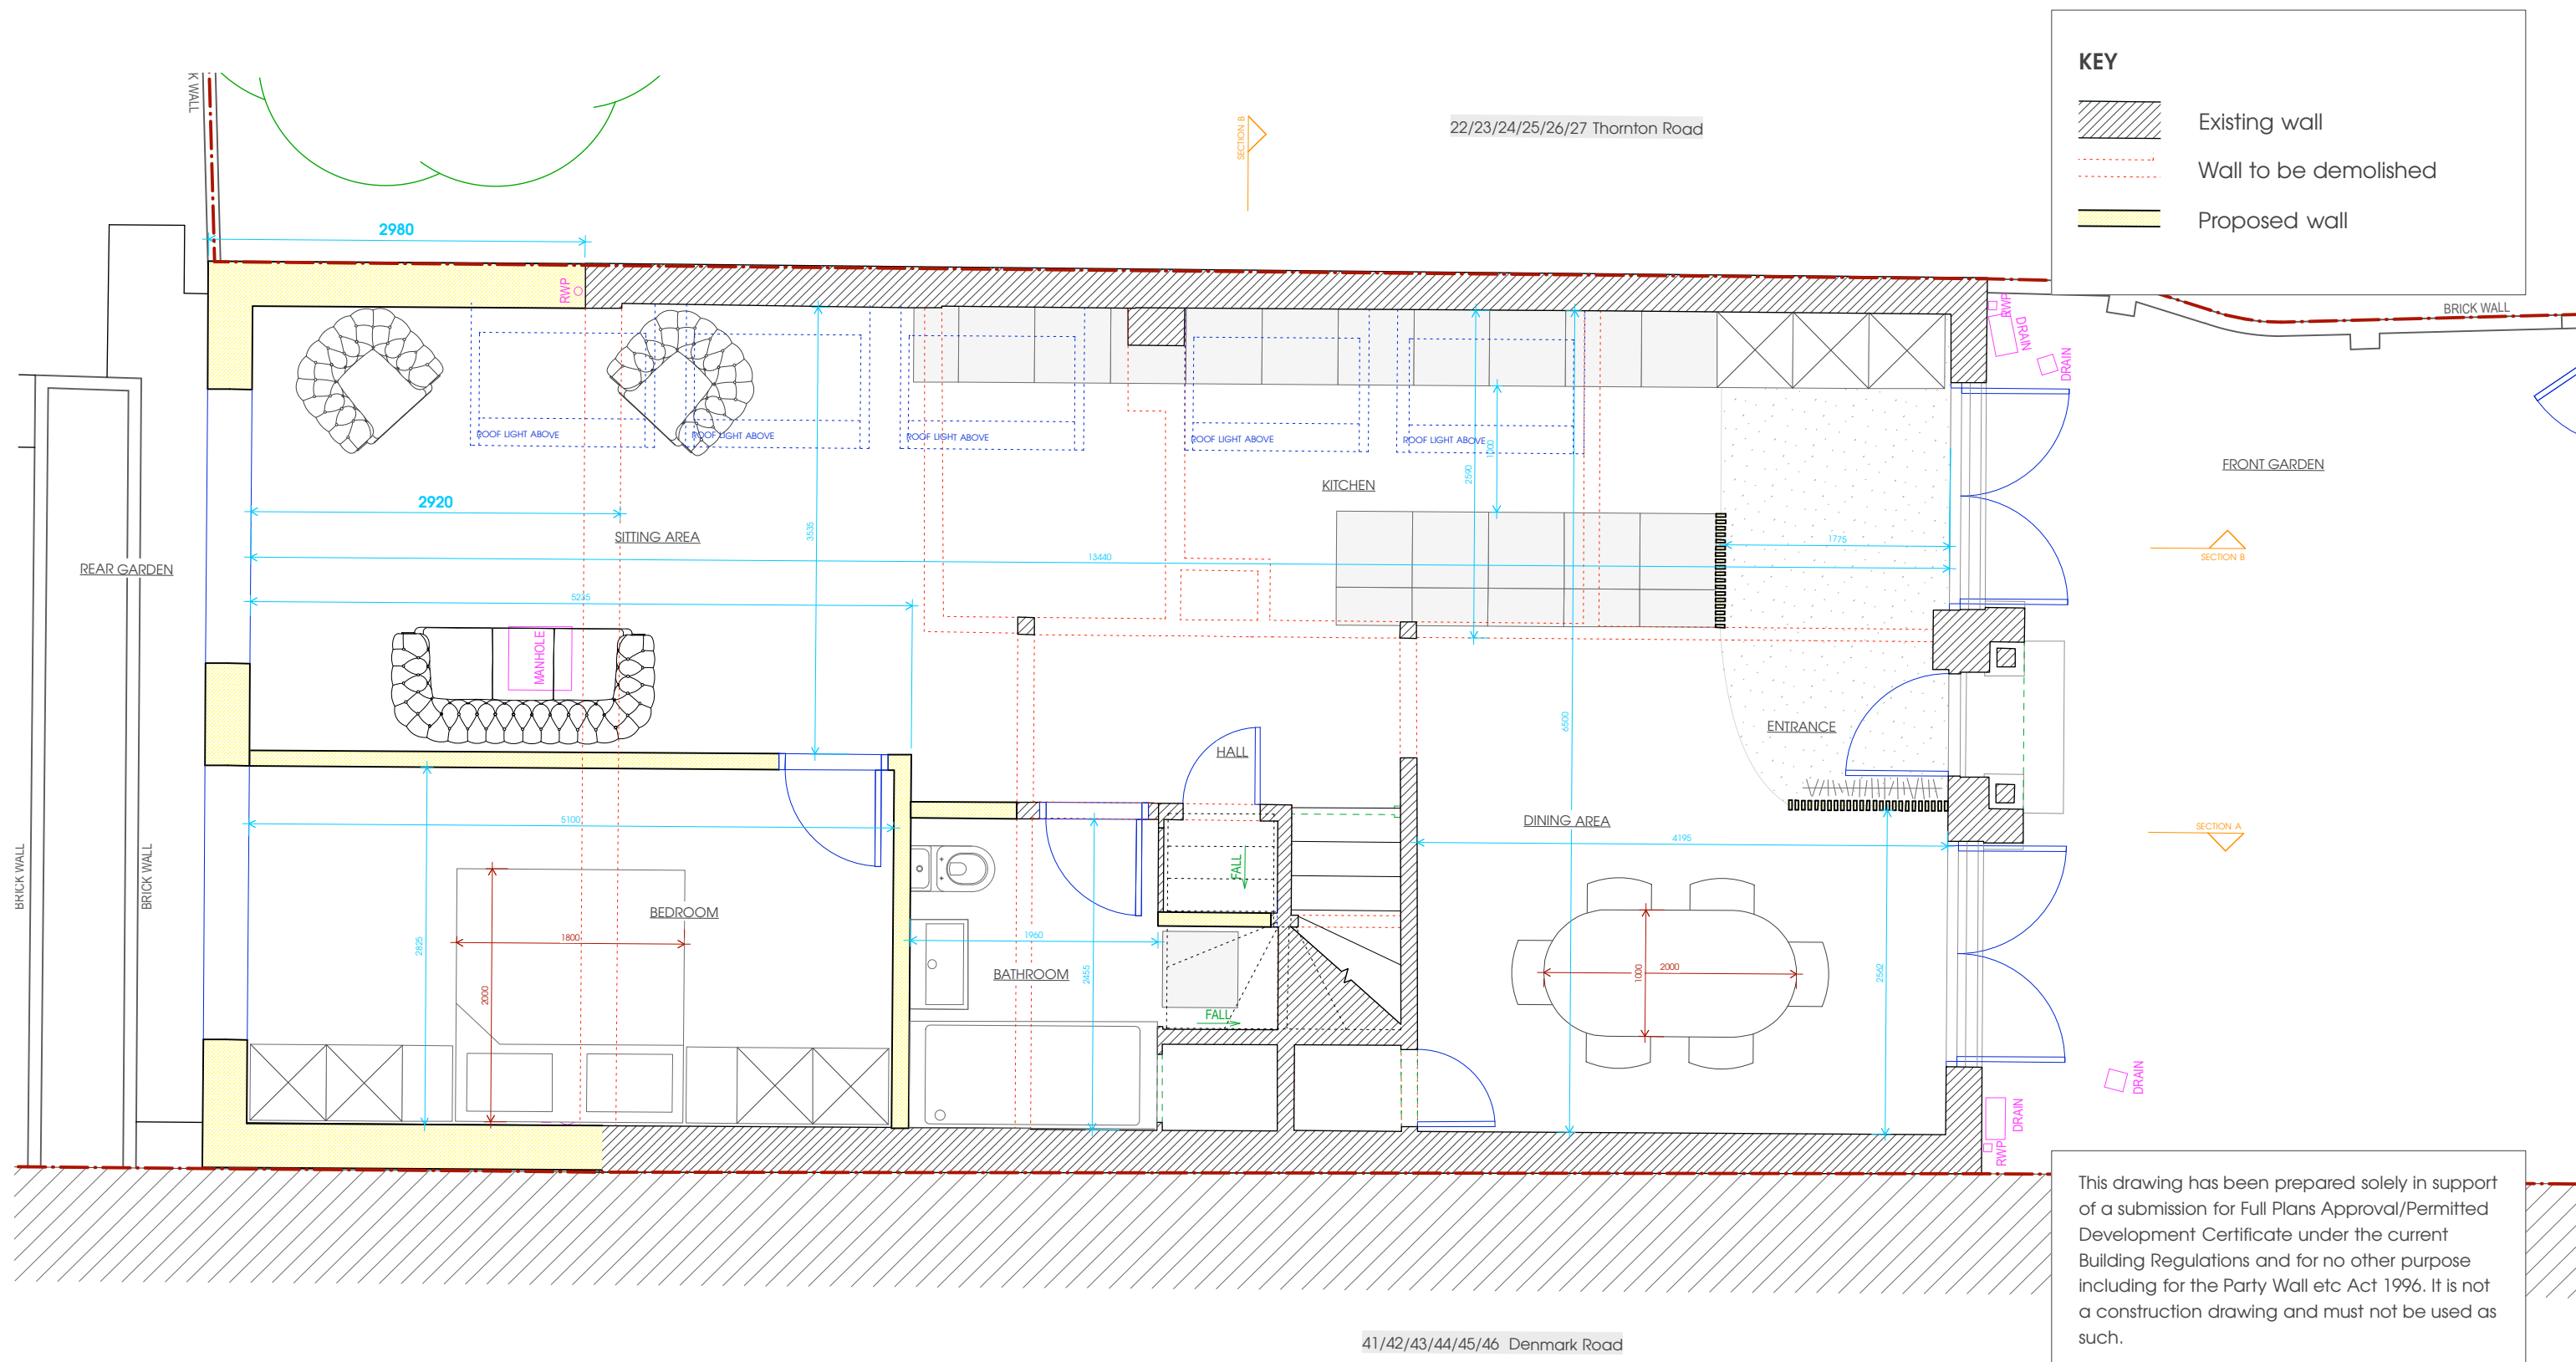

21 Thornton Road

DRAWING Proposed Ground Floor
DWG NO PL_021 REV_planning
SCALE 1:50 @ A3
DRAWN Irene Siljama
CONTACT 8 Effra Parade
London SW2 1PS
07 899 926 731


COPYRIGHT © 2025 Irene Siljama

SECTION B

22/23/24/25/26/27 Thornton Road

KEY

- Existing wall
- Wall to be demolished
- Proposed wall

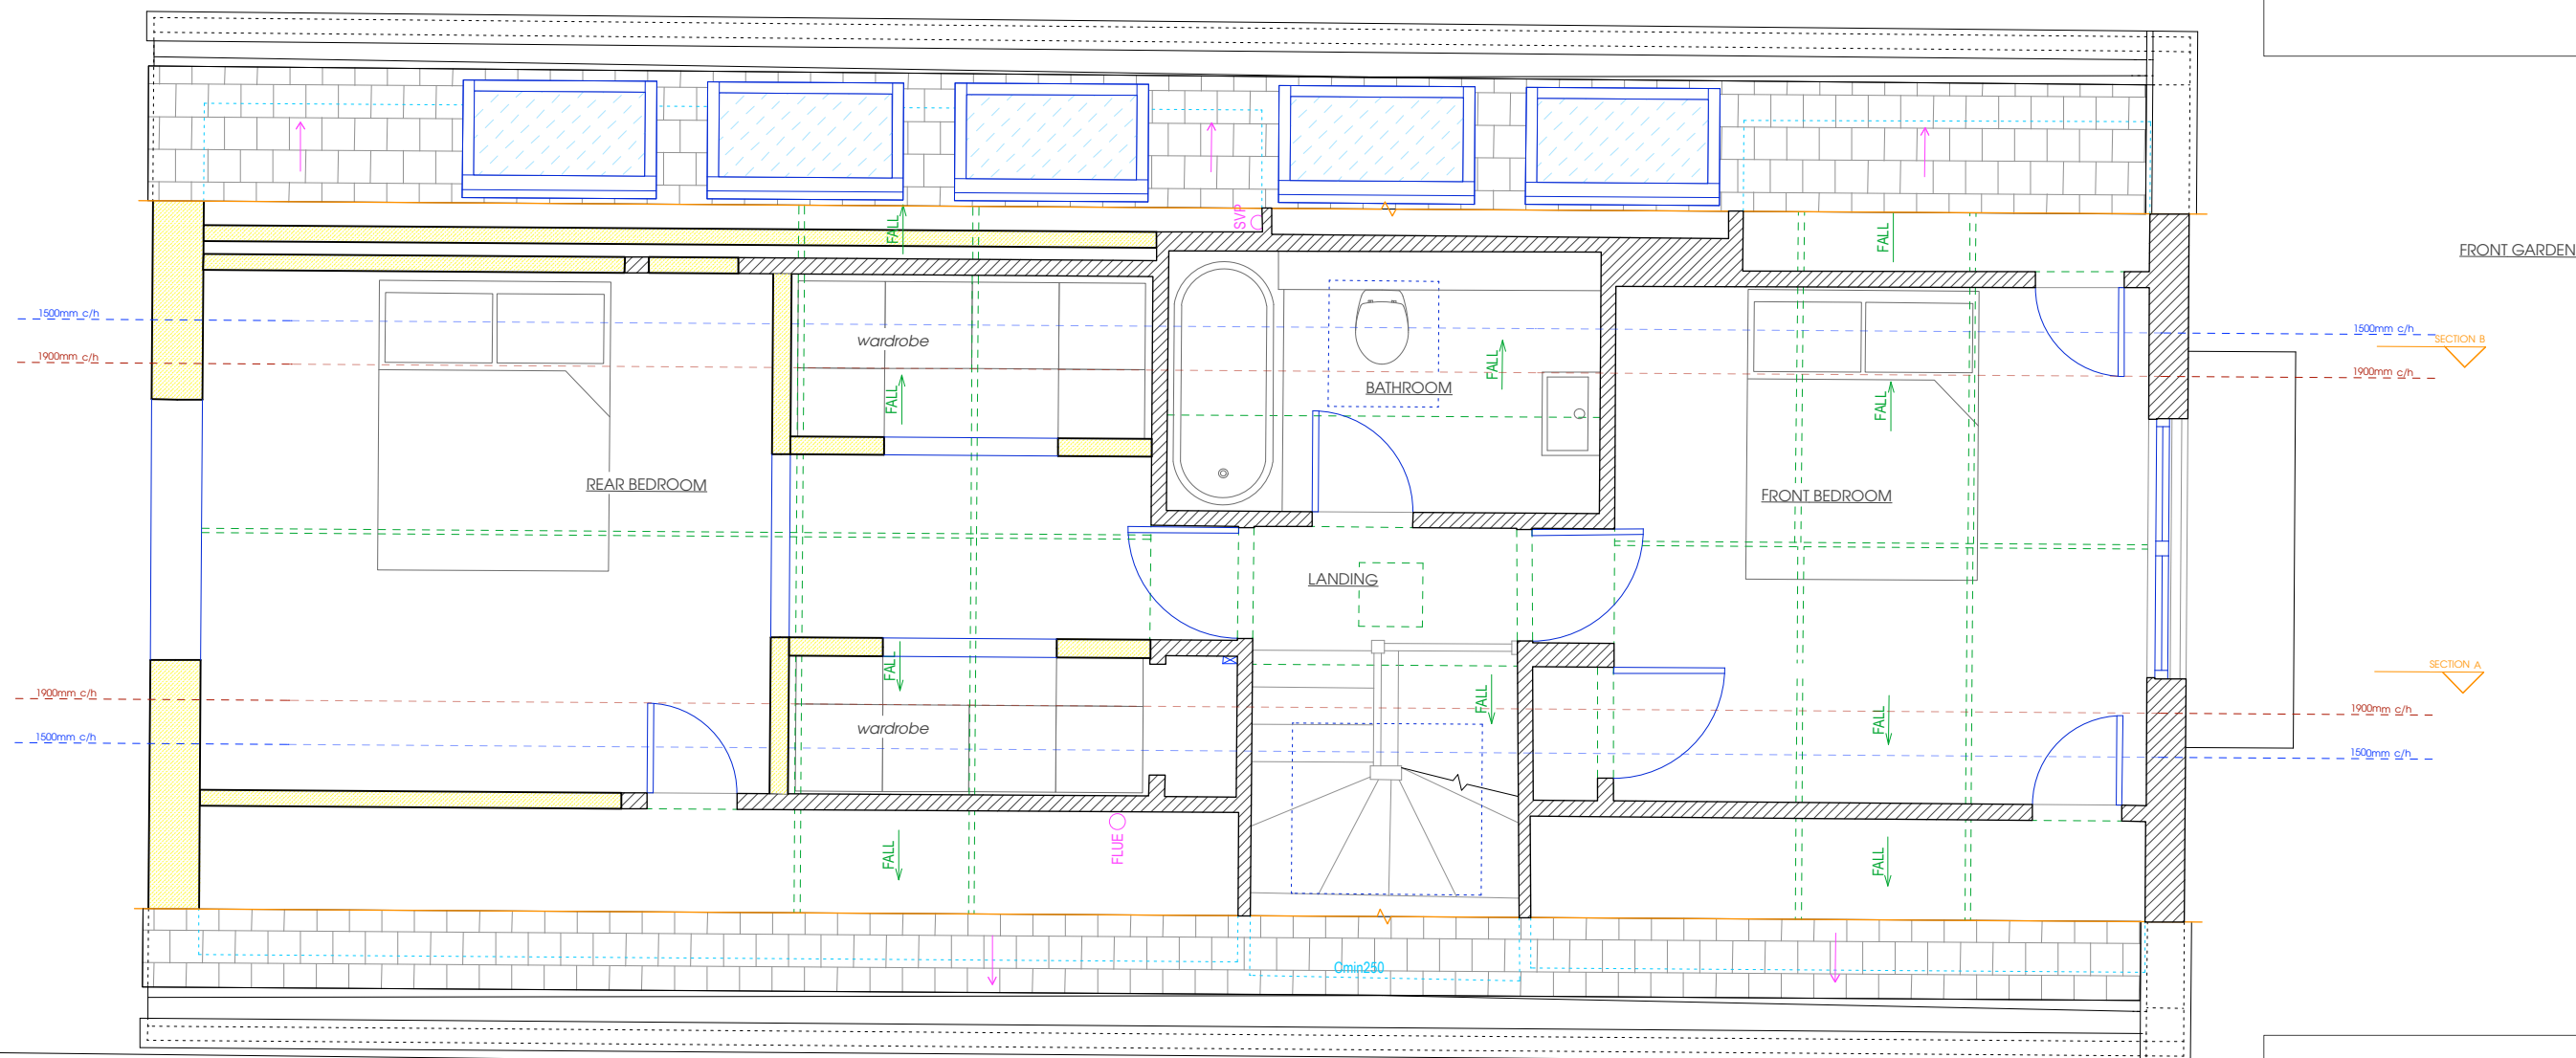


41/42/43/44/45/46 Denmark Road


This drawing has been prepared solely in support of a submission for Full Plans Approval/Permitted Development Certificate under the current Building Regulations and for no other purpose including for the Party Wall etc Act 1996. It is not a construction drawing and must not be used as such.

21 Thornton Road

DRAWING Proposed First Floor
DWG NO PL_022 REV_planning
SCALE 1:50 @ A3
DRAWN Irene Siljama
CONTACT 8 Effra Parade
London SW2 1PS
07 899 926 731

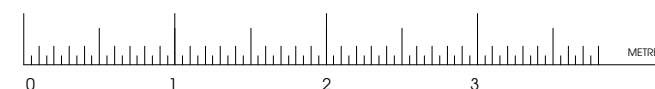

COPYRIGHT © 2025 Irene Siljama

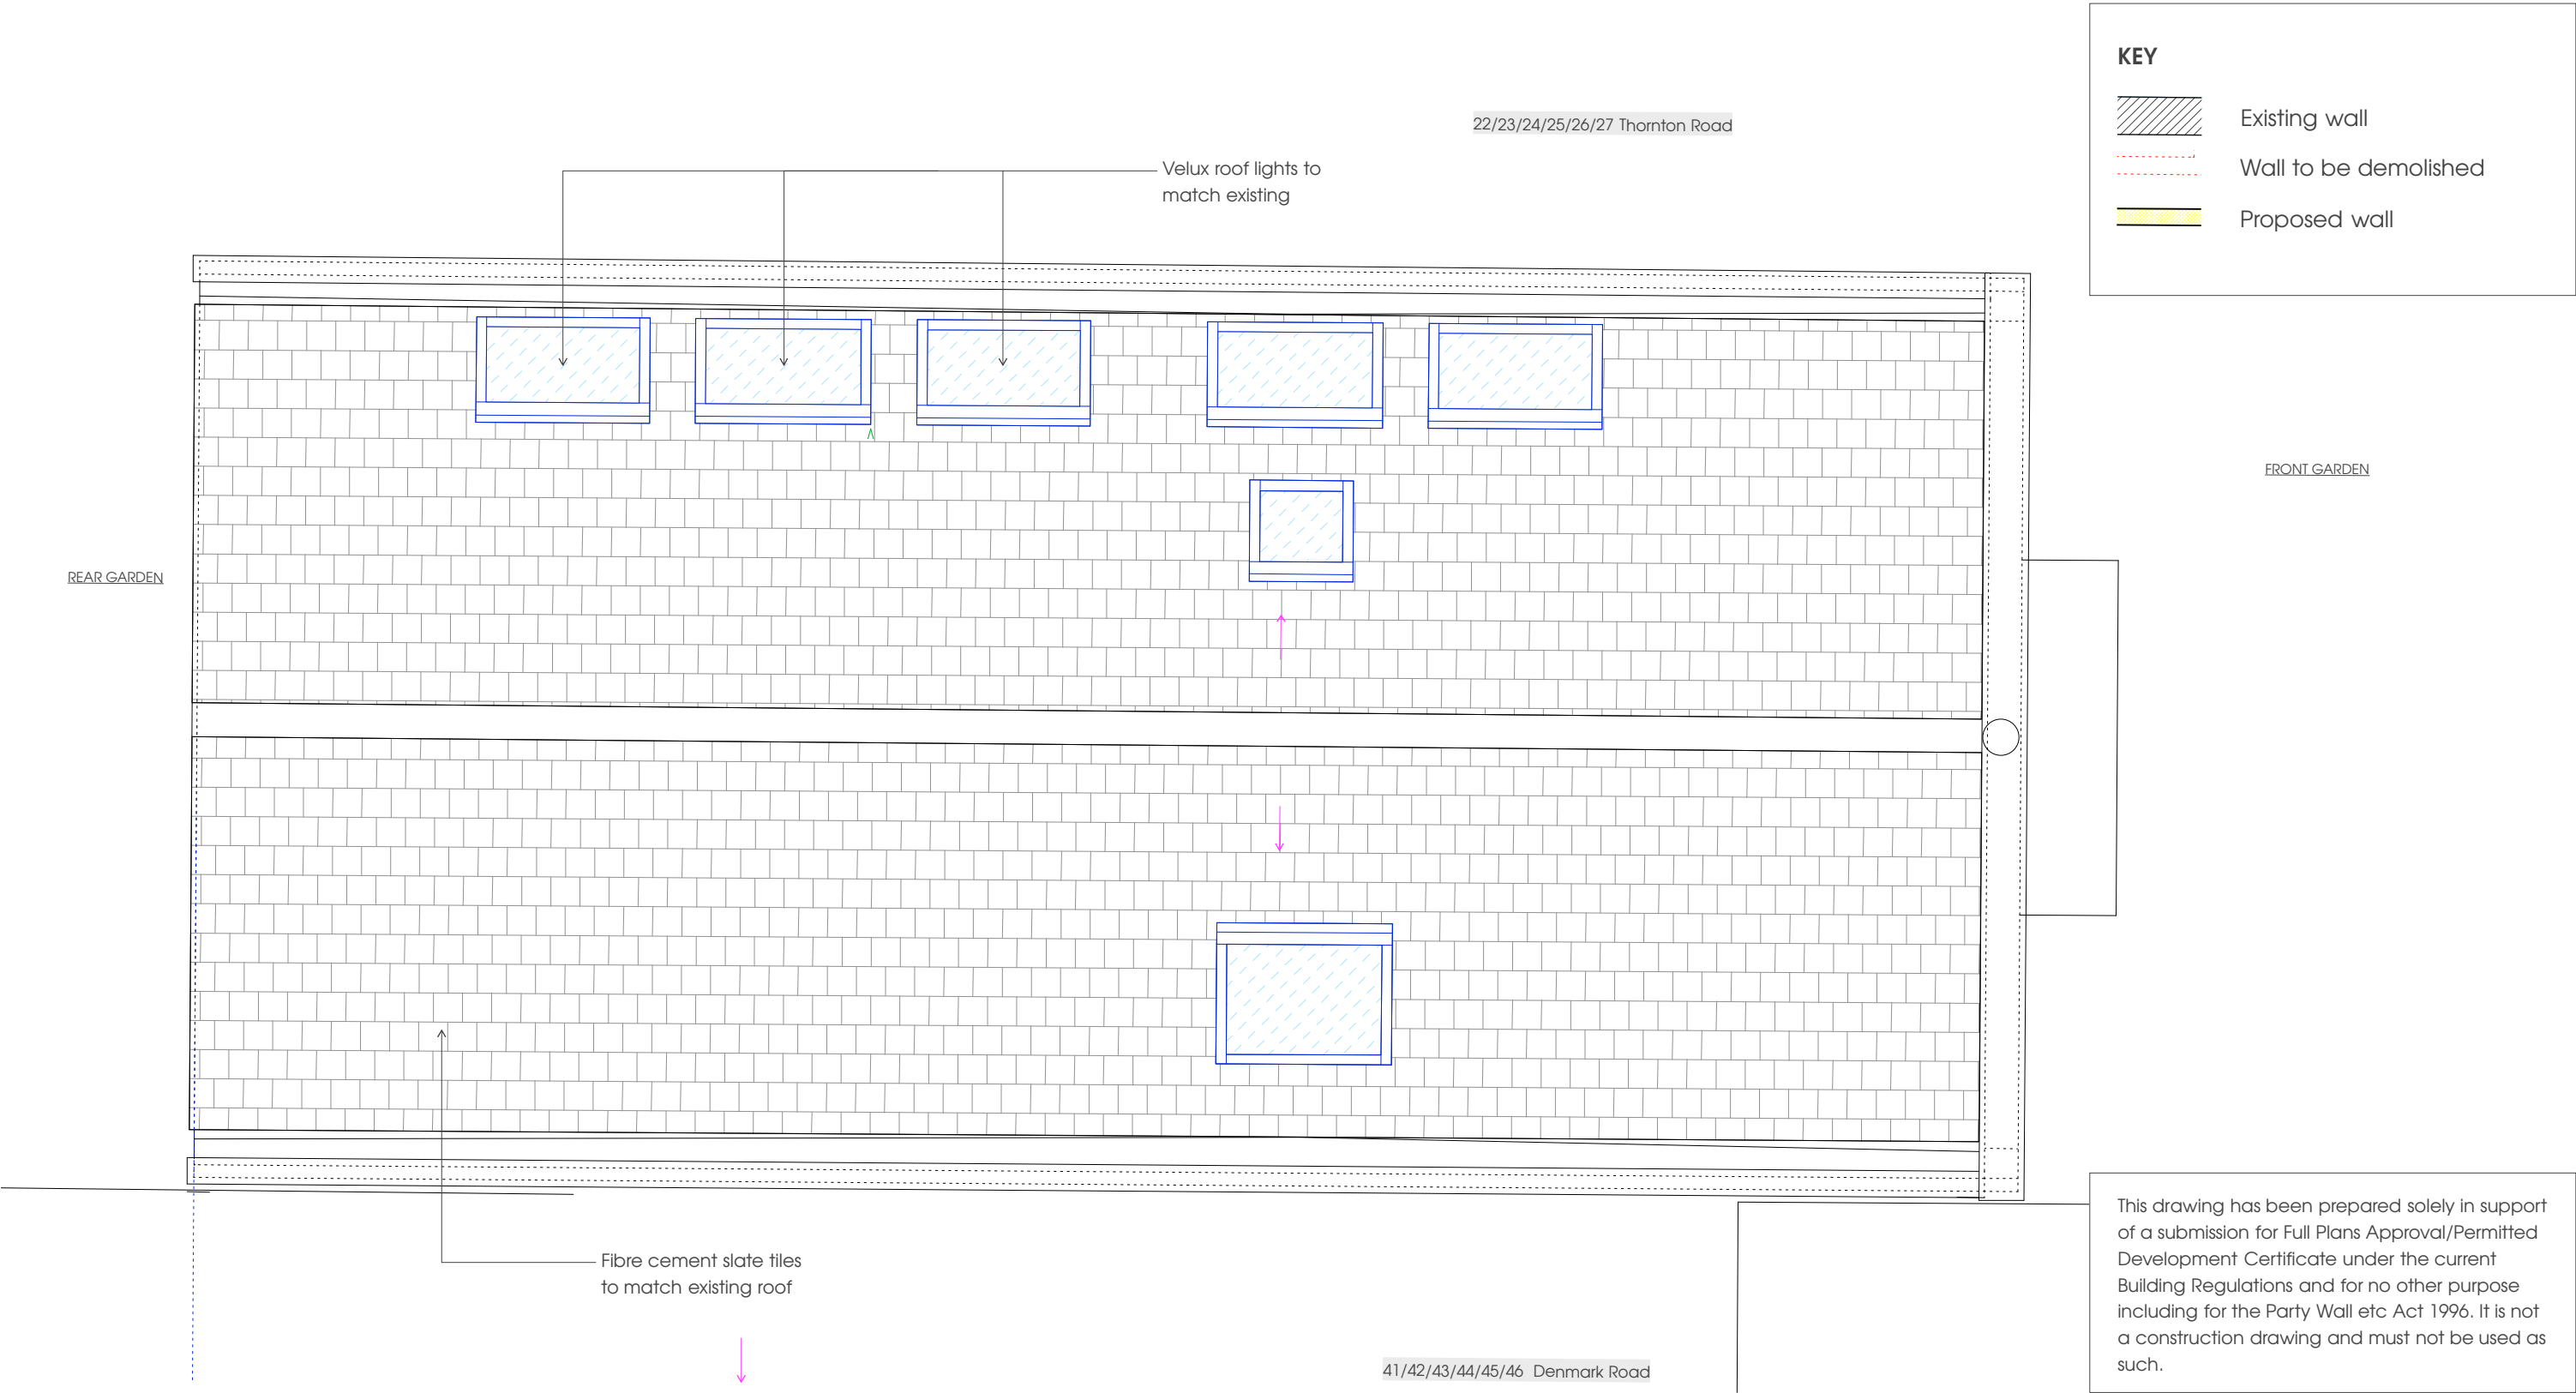


KEY

- Existing wall
- Wall to be demolished
- Proposed wall

This drawing has been prepared solely in support of a submission for Full Plans Approval/Permitted Development Certificate under the current Building Regulations and for no other purpose including for the Party Wall etc Act 1996. It is not a construction drawing and must not be used as such.

21 Thornton Road
DRAWING Proposed Roof
DWG NO PL_024 REV_planning
SCALE 1:50 @ A3
DRAWN Irene Siljama
CONTACT 8 Effra Parade
London SW2 1PS
07 899 926 731



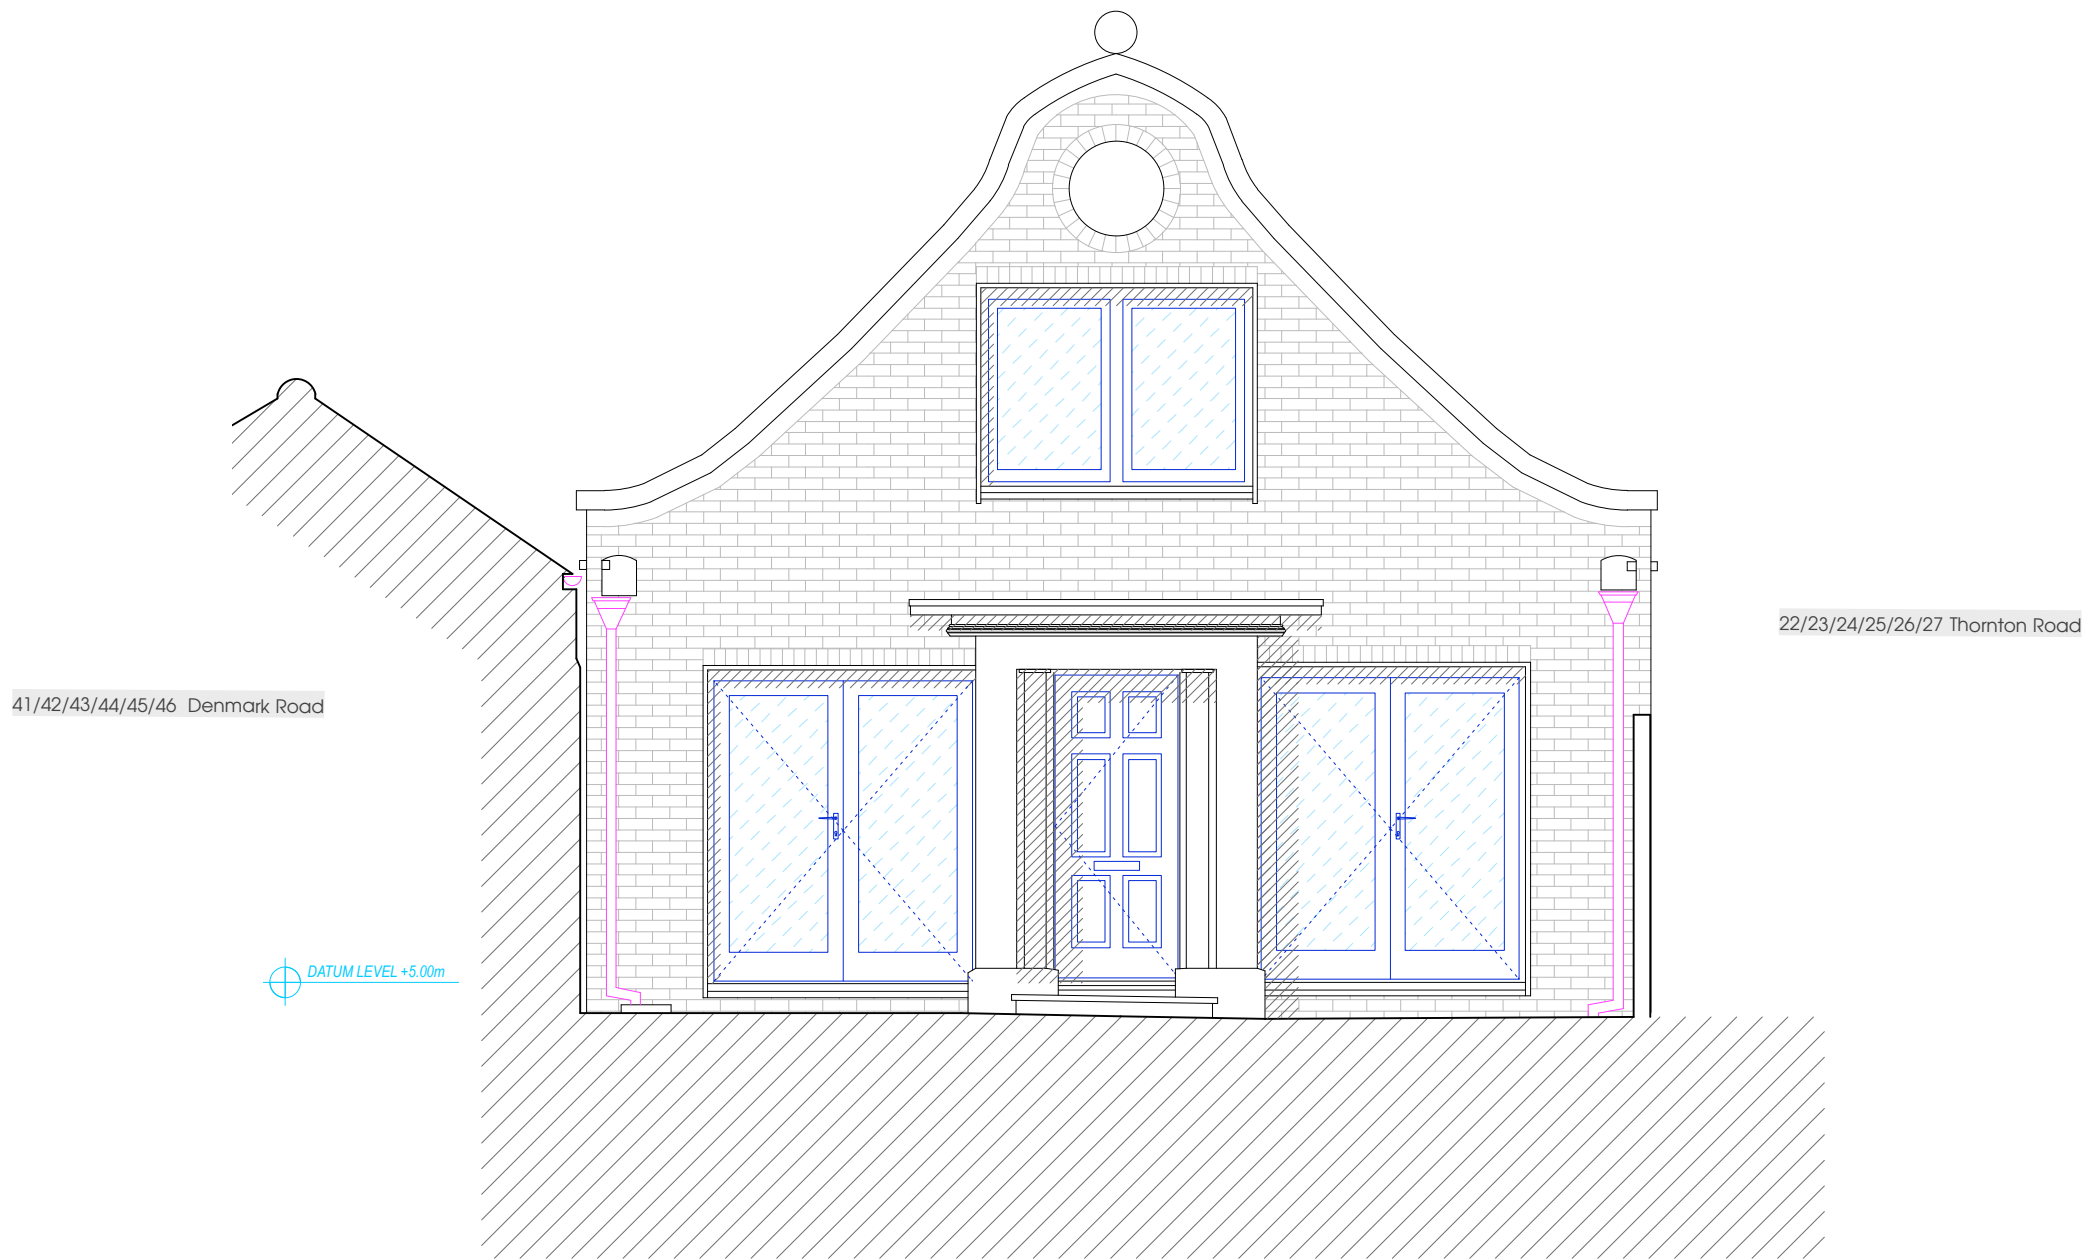

KEY


-  Existing wall
-  Wall to be demolished
-  Proposed wall

This drawing has been prepared solely in support of a submission for Full Plans Approval/Permitted Development Certificate under the current Building Regulations and for no other purpose including for the Party Wall etc Act 1996. It is not a construction drawing and must not be used as such.


21 Thornton Road

DRAWING Proposed Front Elevation
 DWG NO PL_025 REV_planning
 SCALE 1:50 @ A3
 DRAWN Irene Siljama
 CONTACT 8 Effra Parade
 London SW2 1PS
 07 899 926 731



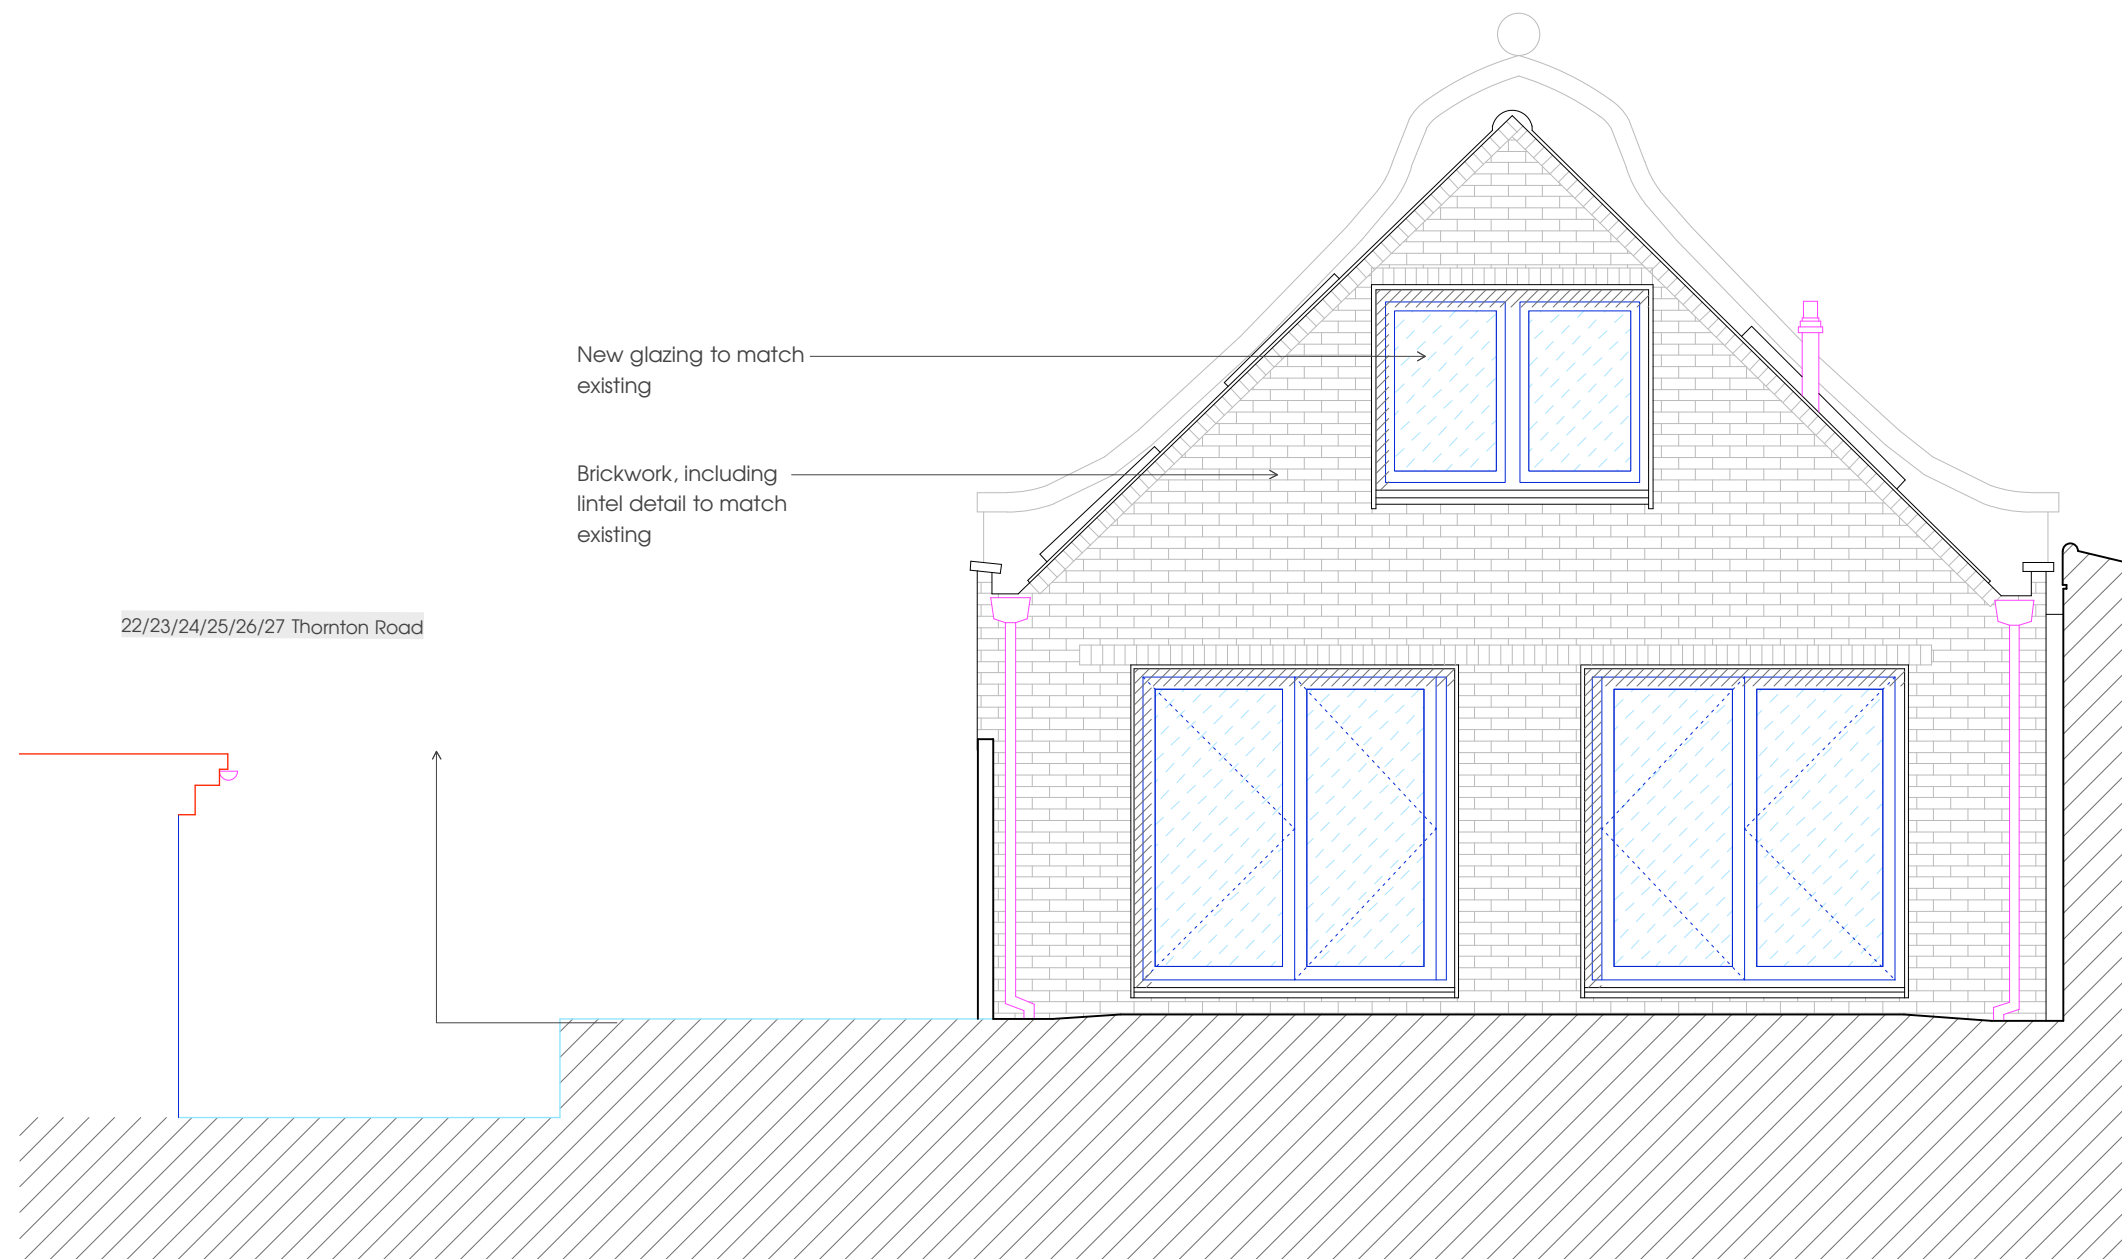

KEY

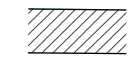-  Existing wall
-  Wall to be demolished
-  Proposed wall

This drawing has been prepared solely in support of a submission for Full Plans Approval/Permitted Development Certificate under the current Building Regulations and for no other purpose including for the Party Wall etc Act 1996. It is not a construction drawing and must not be used as such.

21 Thornton Road

DRAWING Proposed Elevation
DWG NO PL_026 REV_planning
SCALE 1:50 @ A3
DRAWN Irene Siljama
CONTACT 8 Effra Parade
London SW2 1PS
07 899 926 731


COPYRIGHT © 2025 Irene Siljama

KEY

Existing wall

Wall to be demolished

Proposed wall

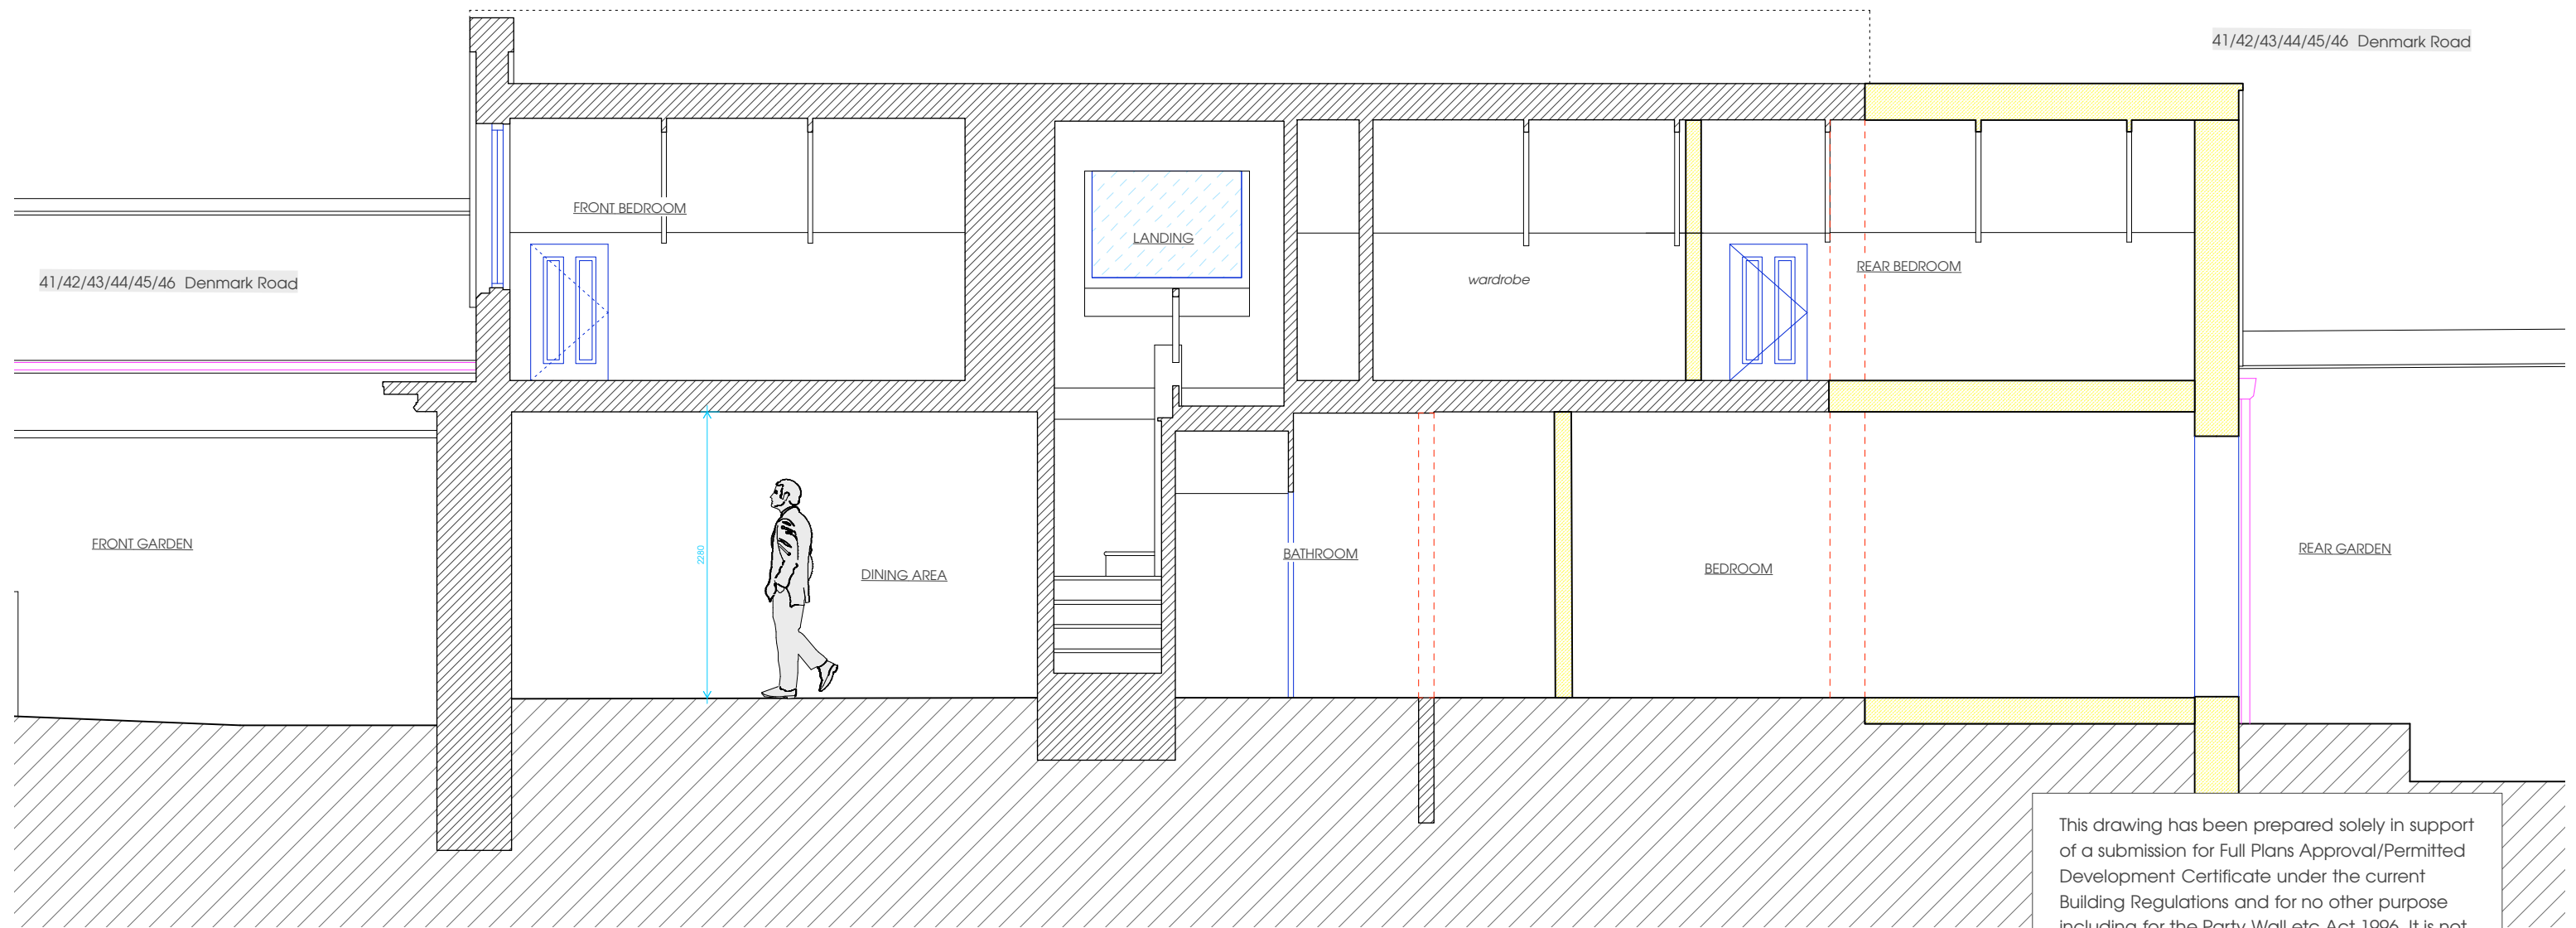

This drawing has been prepared solely in support of a submission for Full Plans Approval/Permitted Development Certificate under the current Building Regulations and for no other purpose including for the Party Wall etc Act 1996. It is not a construction drawing and must not be used as such.

21 Thornton Road

DRAWING

Proposed Section A

DWG NO

PL_027

REV_planning

SCALE

1:50 @ A3

DRAWN

Irene Siljama


CONTACT

8 Effra Parade

London SW2 1PS

07 899 926 731

COPYRIGHT © 2025 Irene Siljama

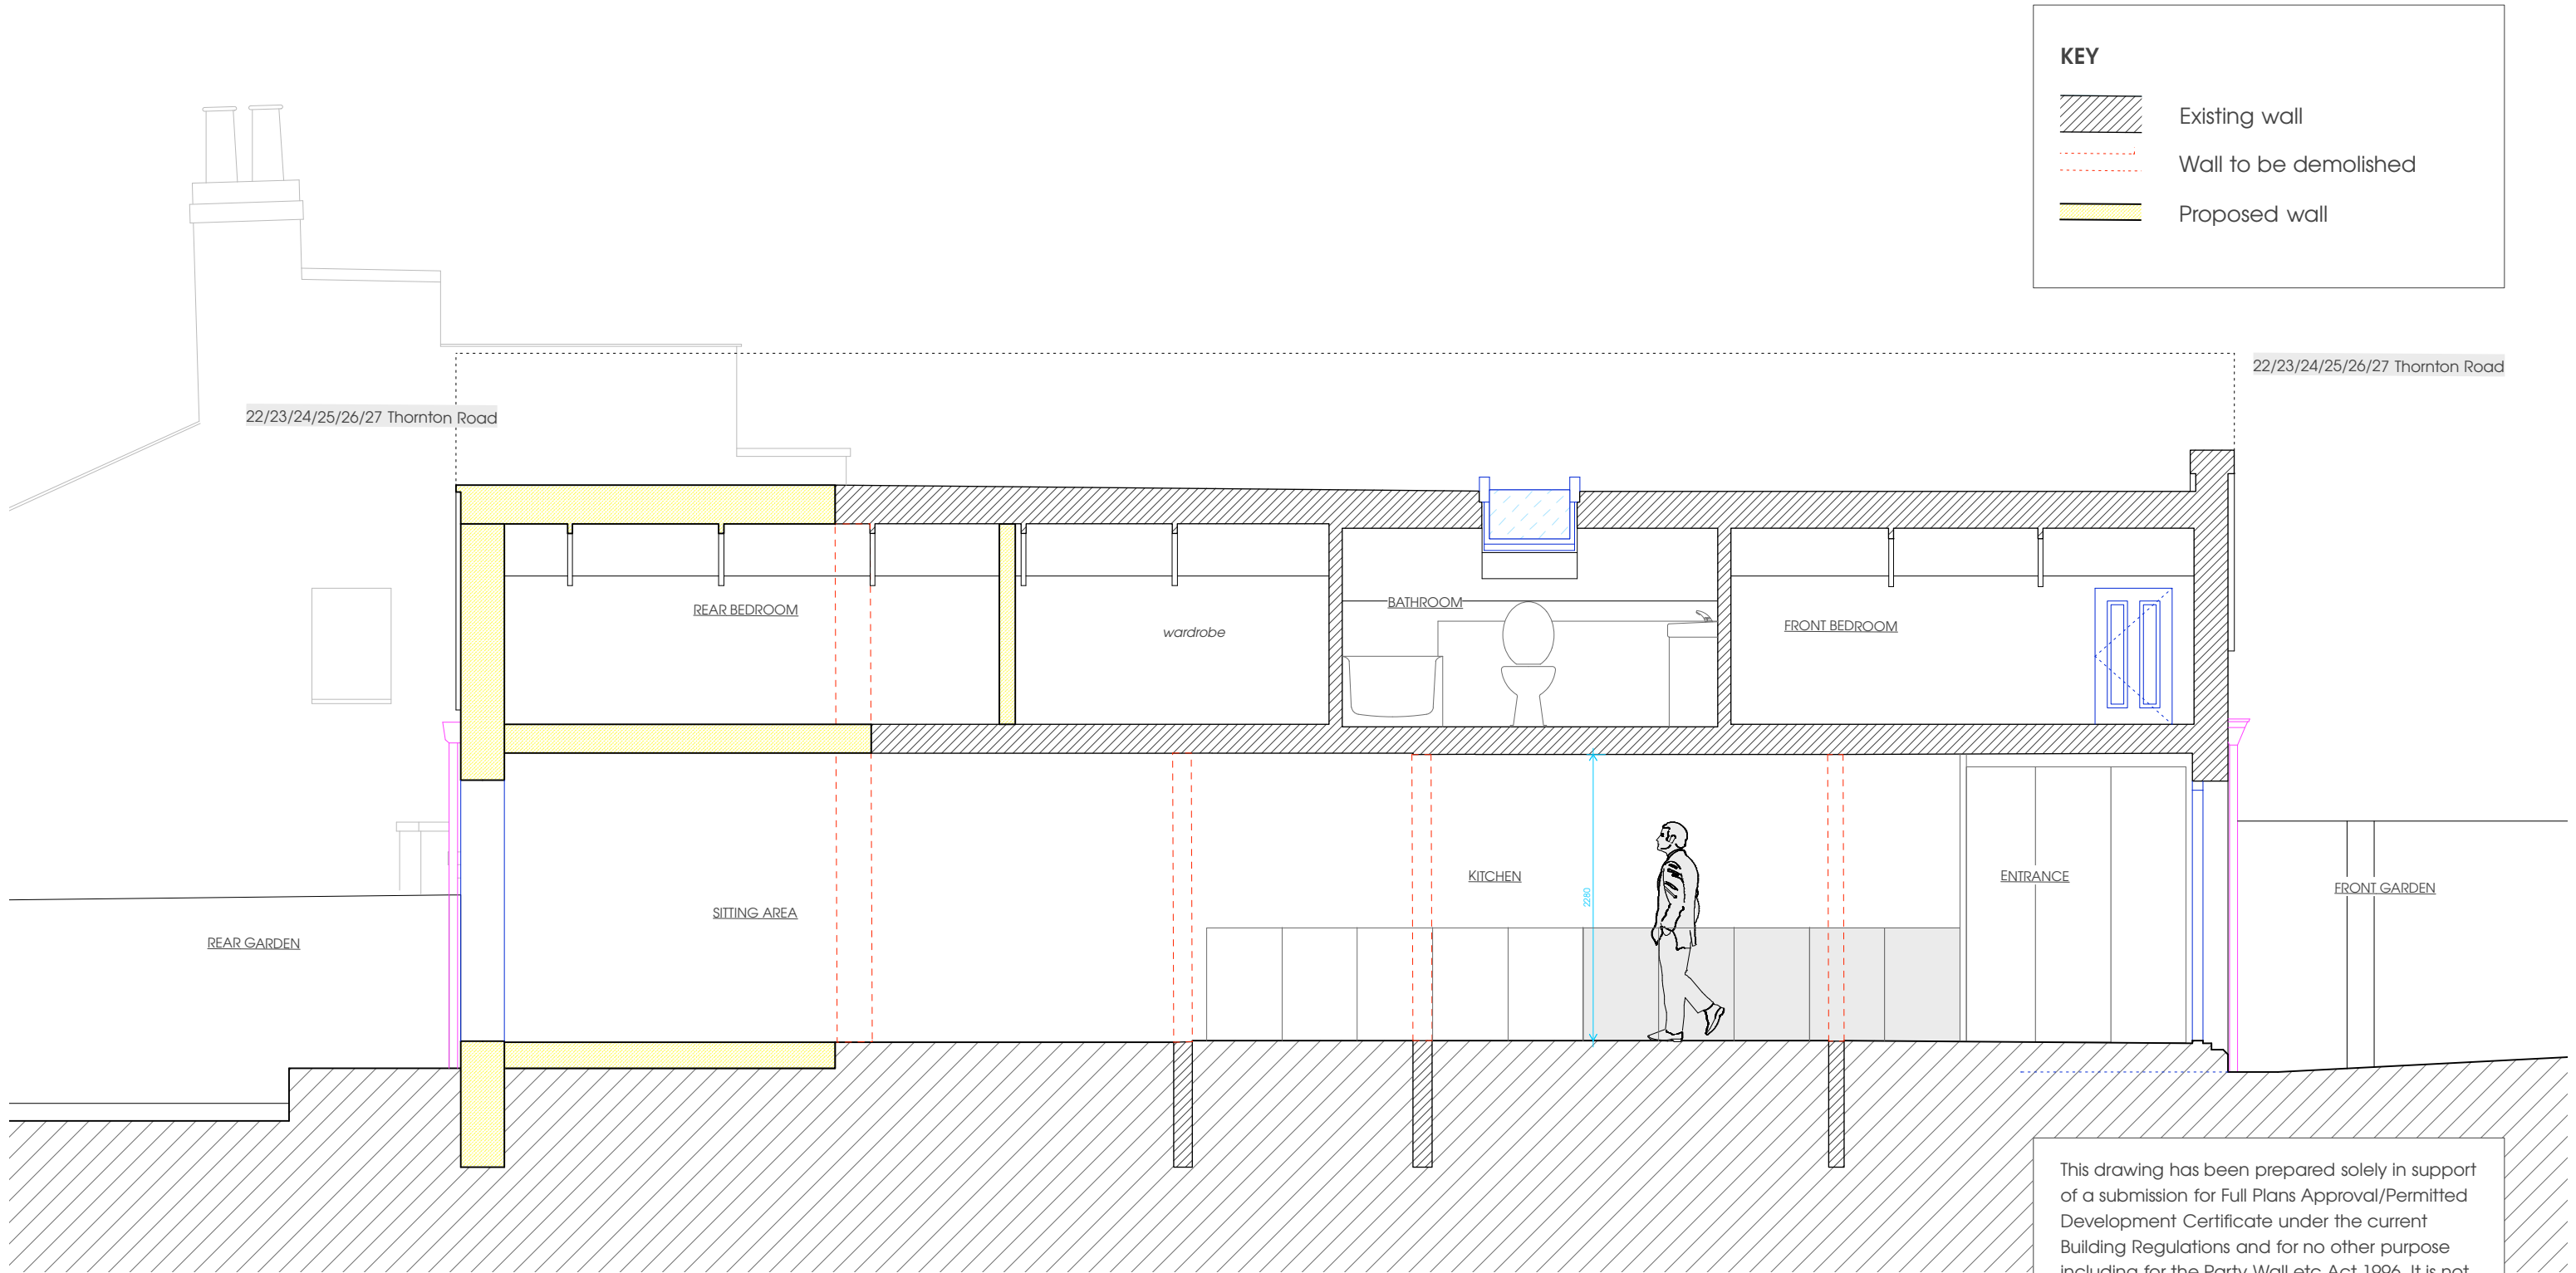


KEY

- Existing wall
- Wall to be demolished
- Proposed wall

This drawing has been prepared solely in support of a submission for Full Plans Approval/Permitted Development Certificate under the current Building Regulations and for no other purpose including for the Party Wall etc Act 1996. It is not a construction drawing and must not be used as such.

21 Thornton Road

DRAWING Proposed Section B
DWG NO PL_028 REV_planning
SCALE 1:50 @ A3
DRAWN Irene Siljama
CONTACT 8 Effra Parade
London SW2 1PS
07 899 926 731

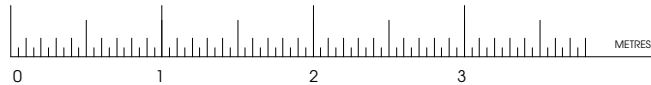


KEY

Existing wall

Wall to be demolished

Proposed wall

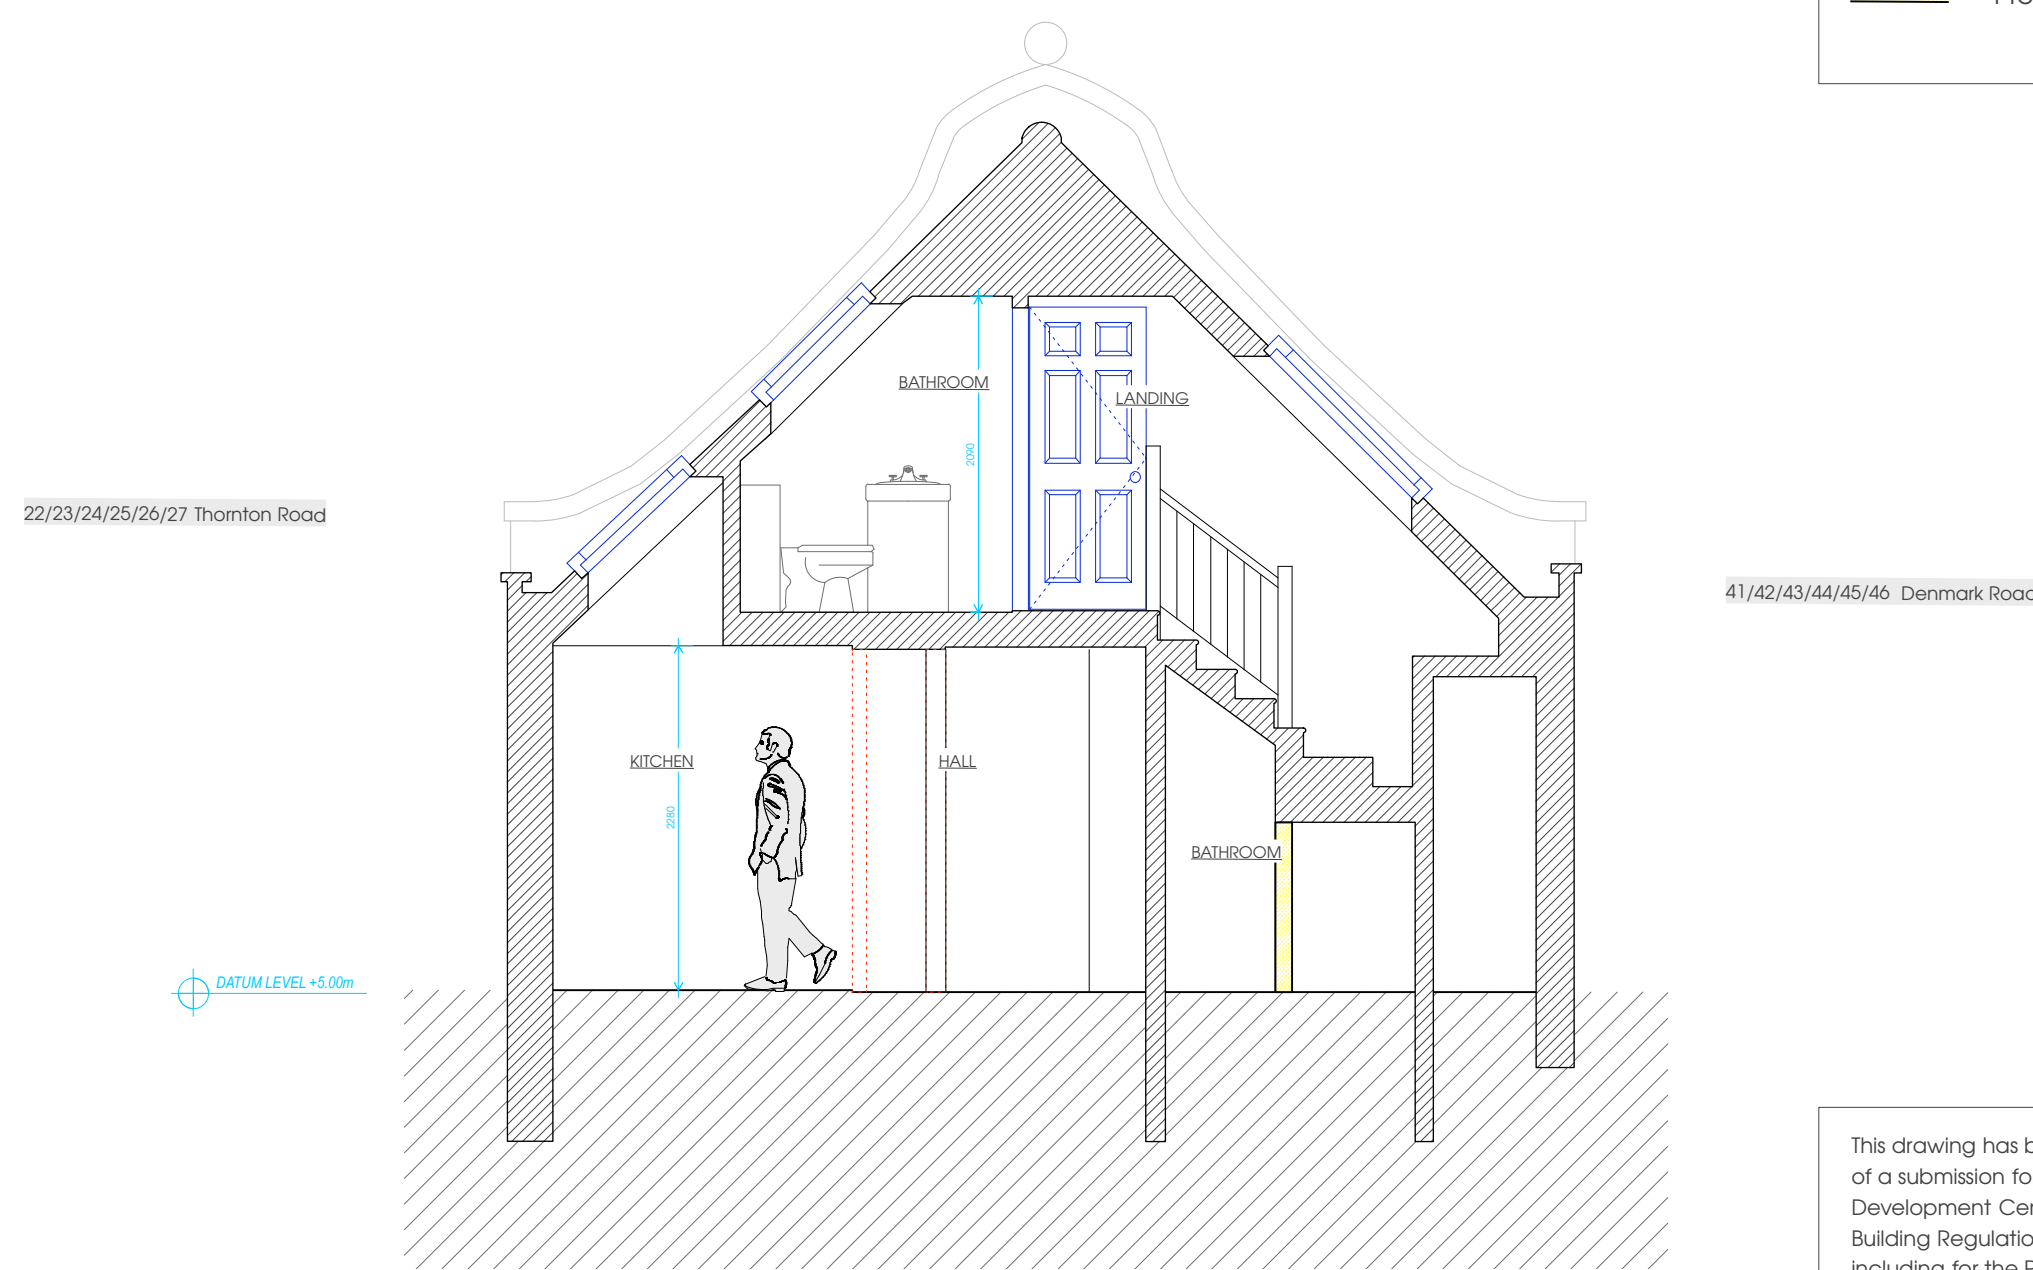

This drawing has been prepared solely in support of a submission for Full Plans Approval/Permitted Development Certificate under the current Building Regulations and for no other purpose including for the Party Wall etc Act 1996. It is not a construction drawing and must not be used as such.

21 Thornton Road

DRAWING

Proposed Section C

DWG NO

PL_029

REV_planning

SCALE

1:50 @ A3

DRAWN

Irene Siljama

CONTACT

8 Effra Parade

London SW2 1PS

07 899 926 731

